




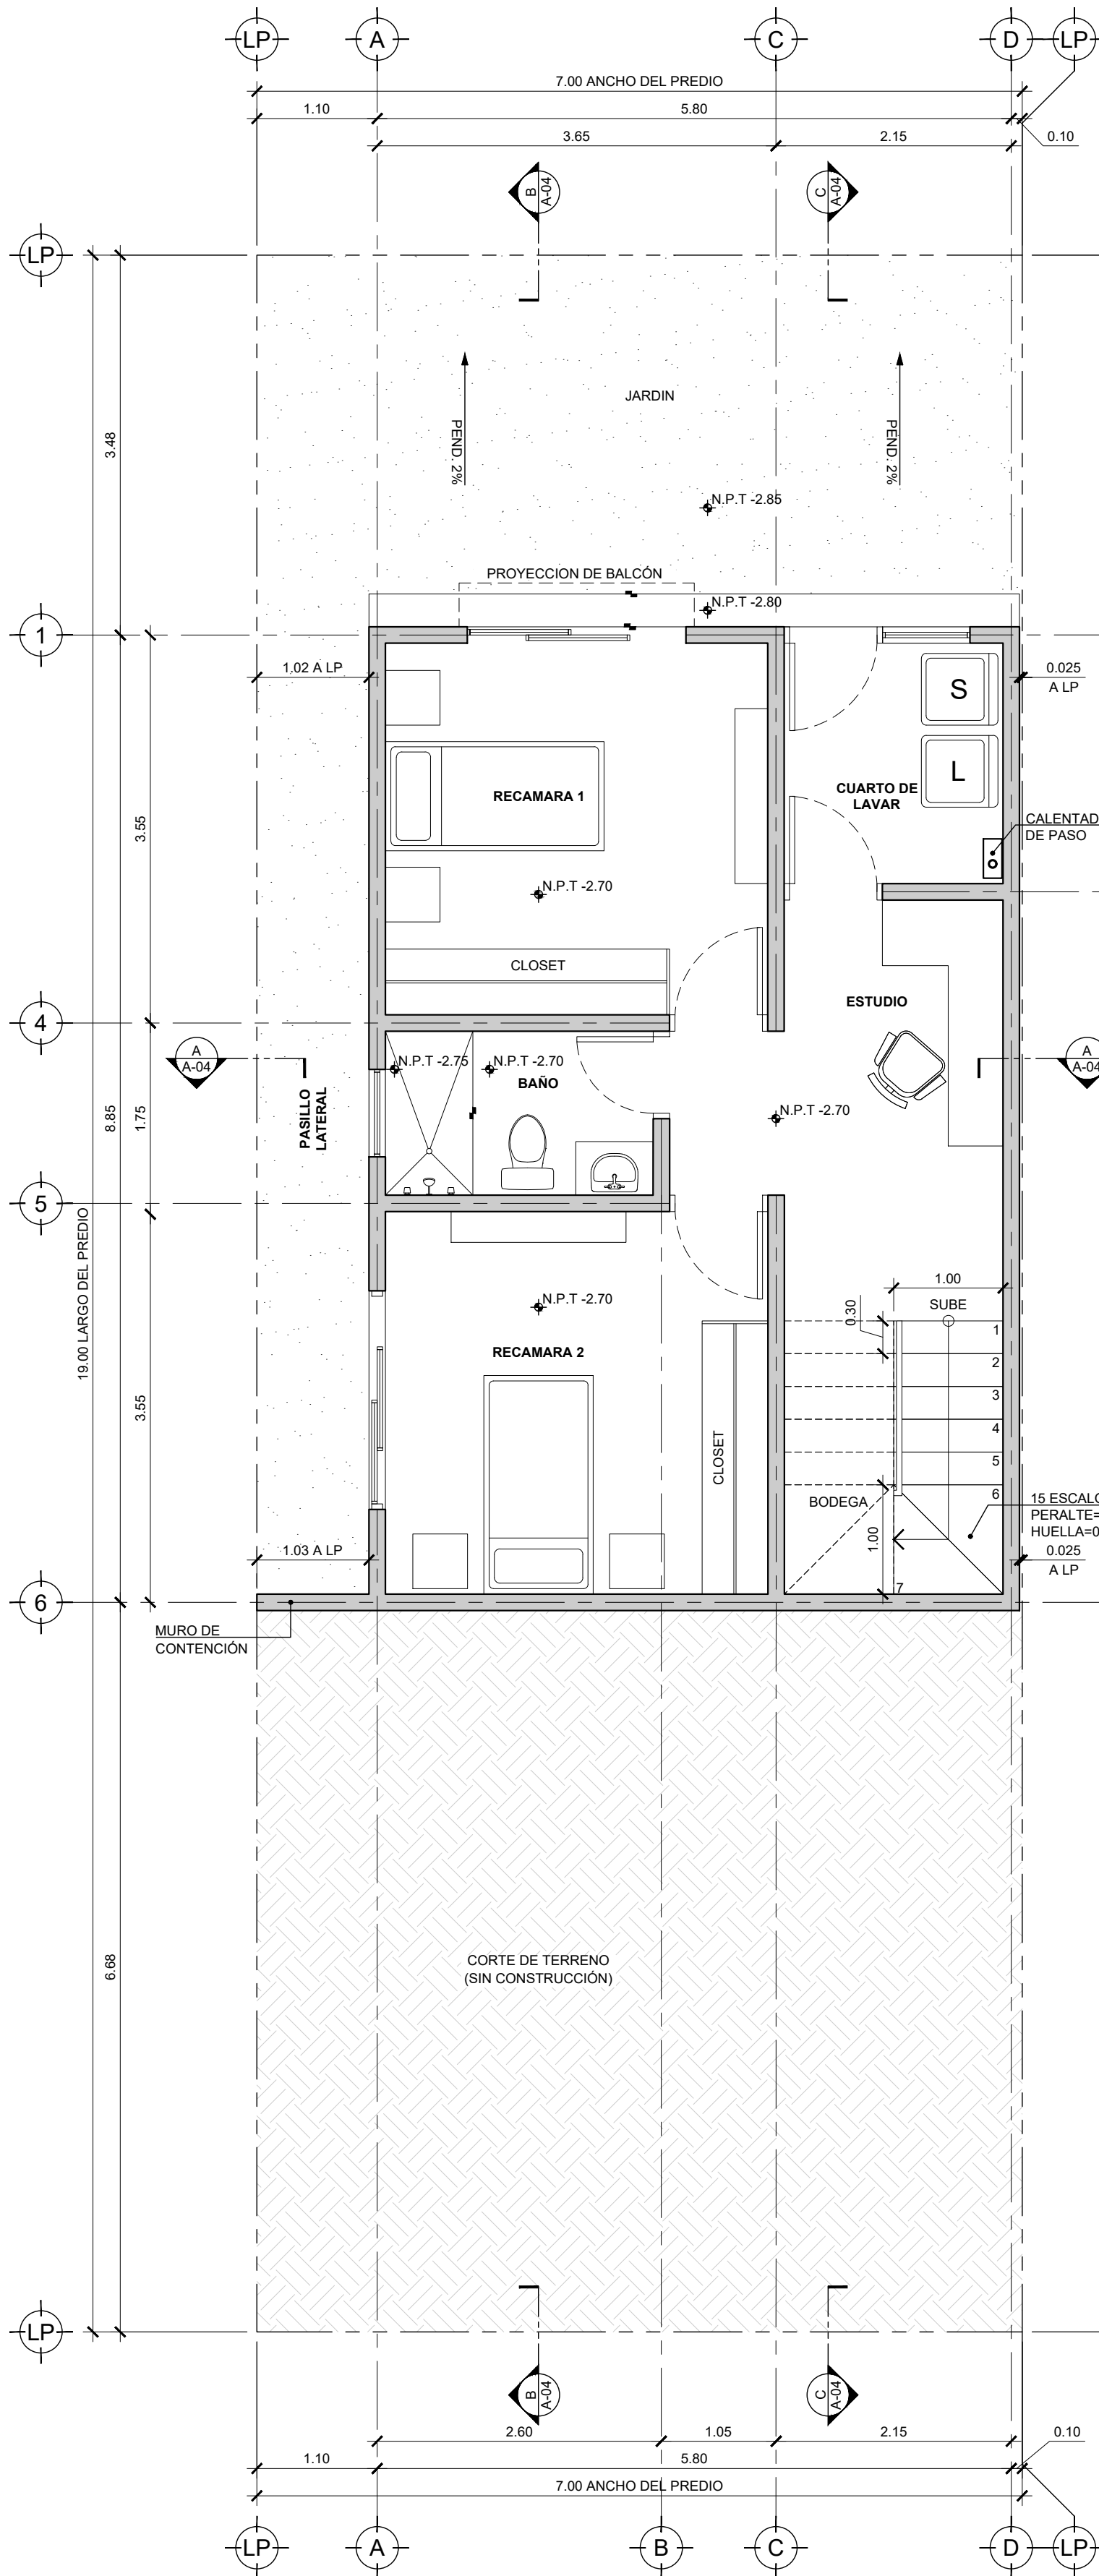

PLANTA NIVEL -1
ESC 1:50

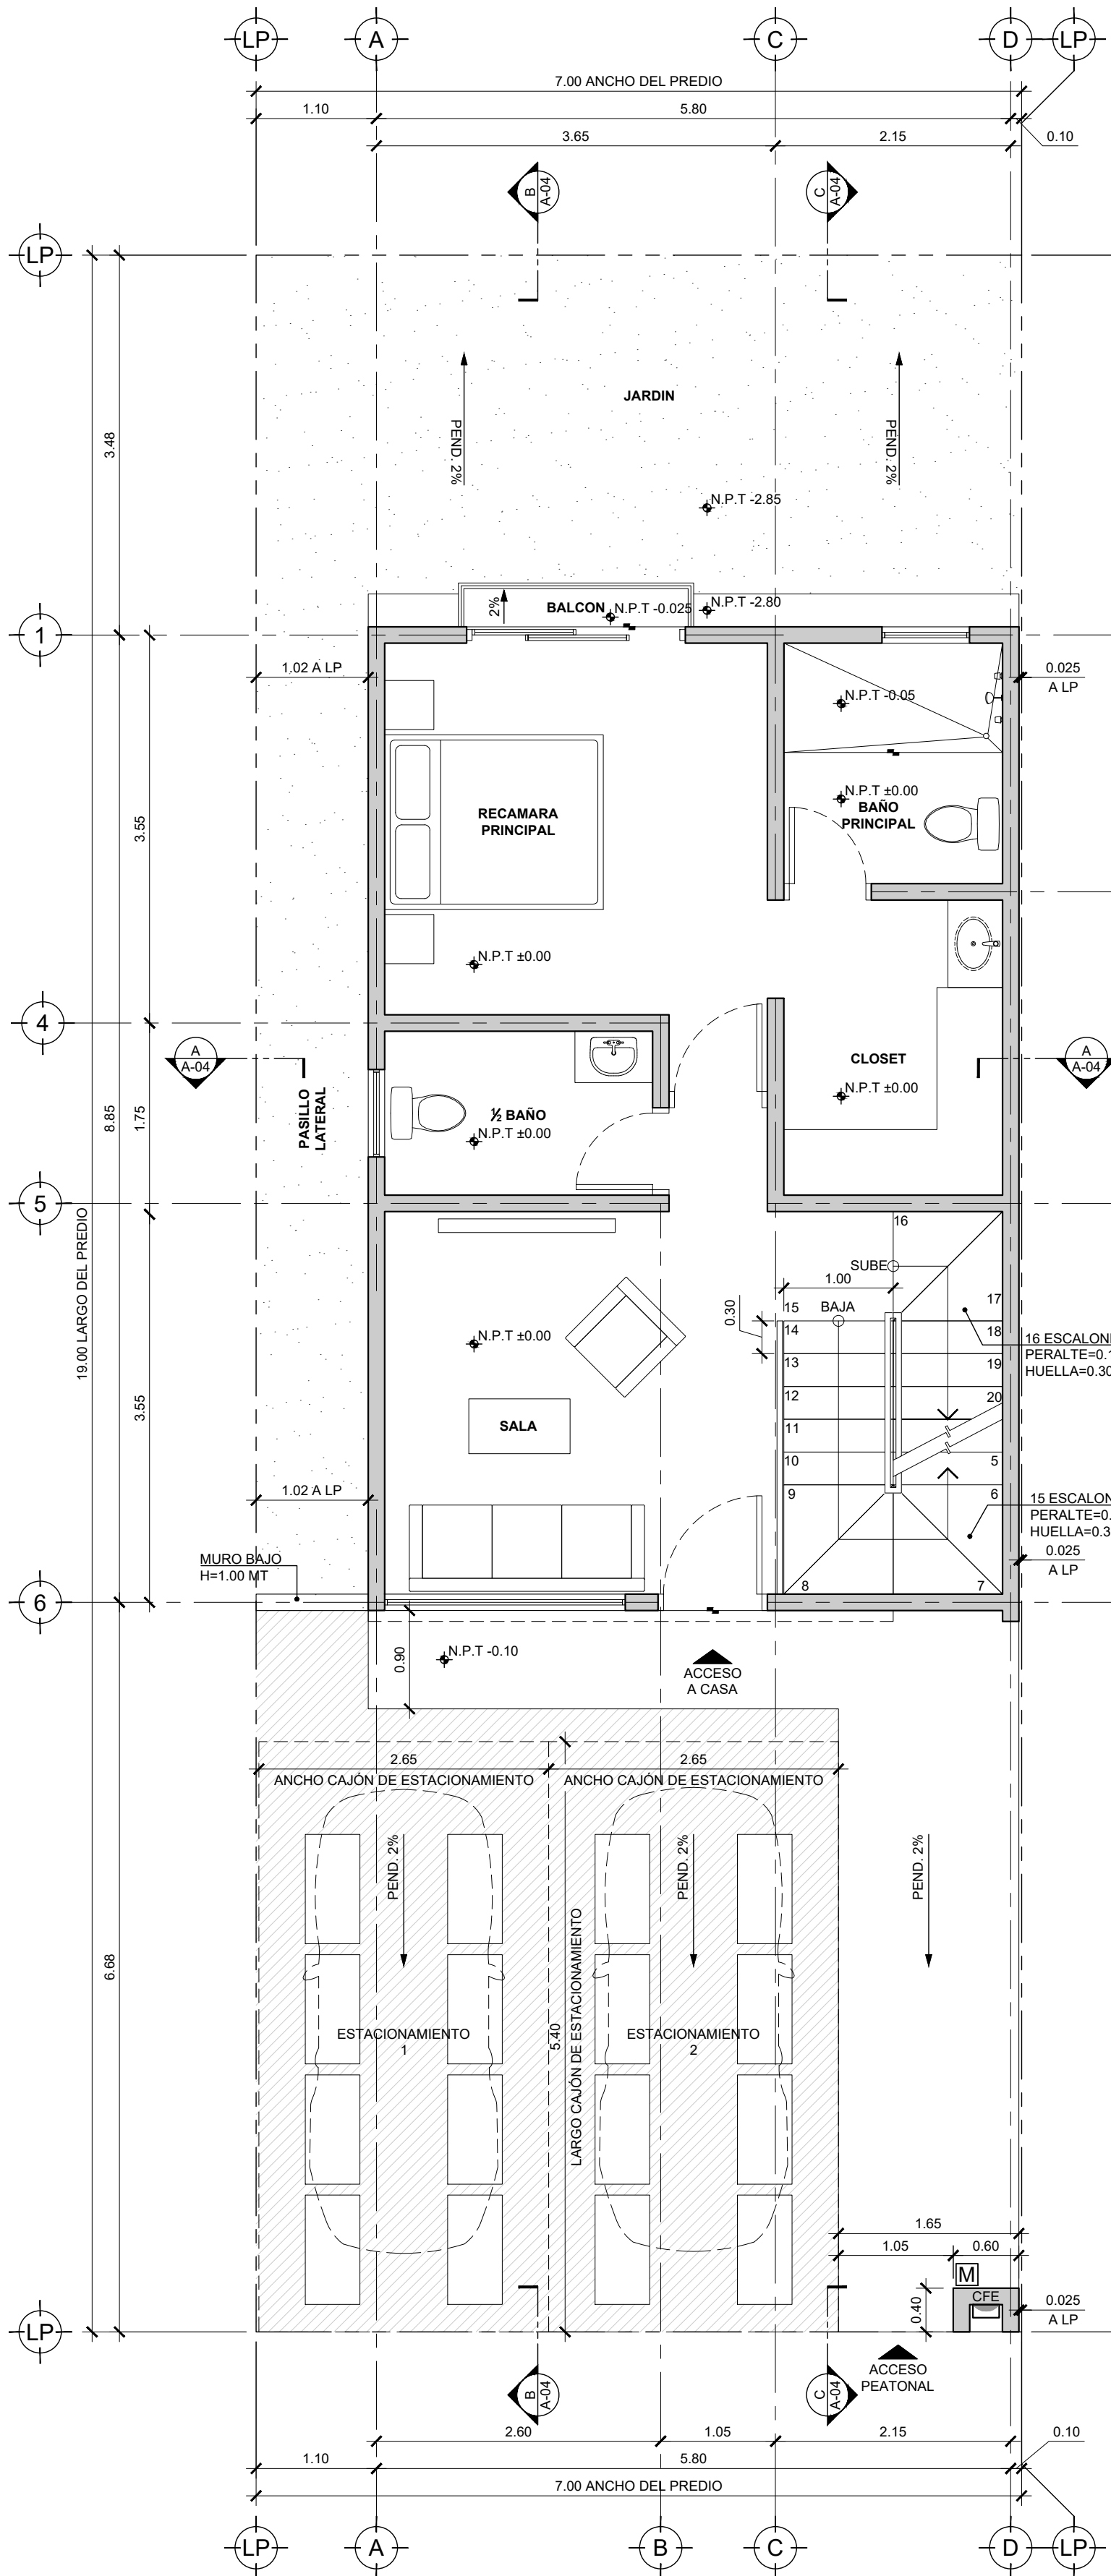

PLANTA BAJA
ESC 1:50

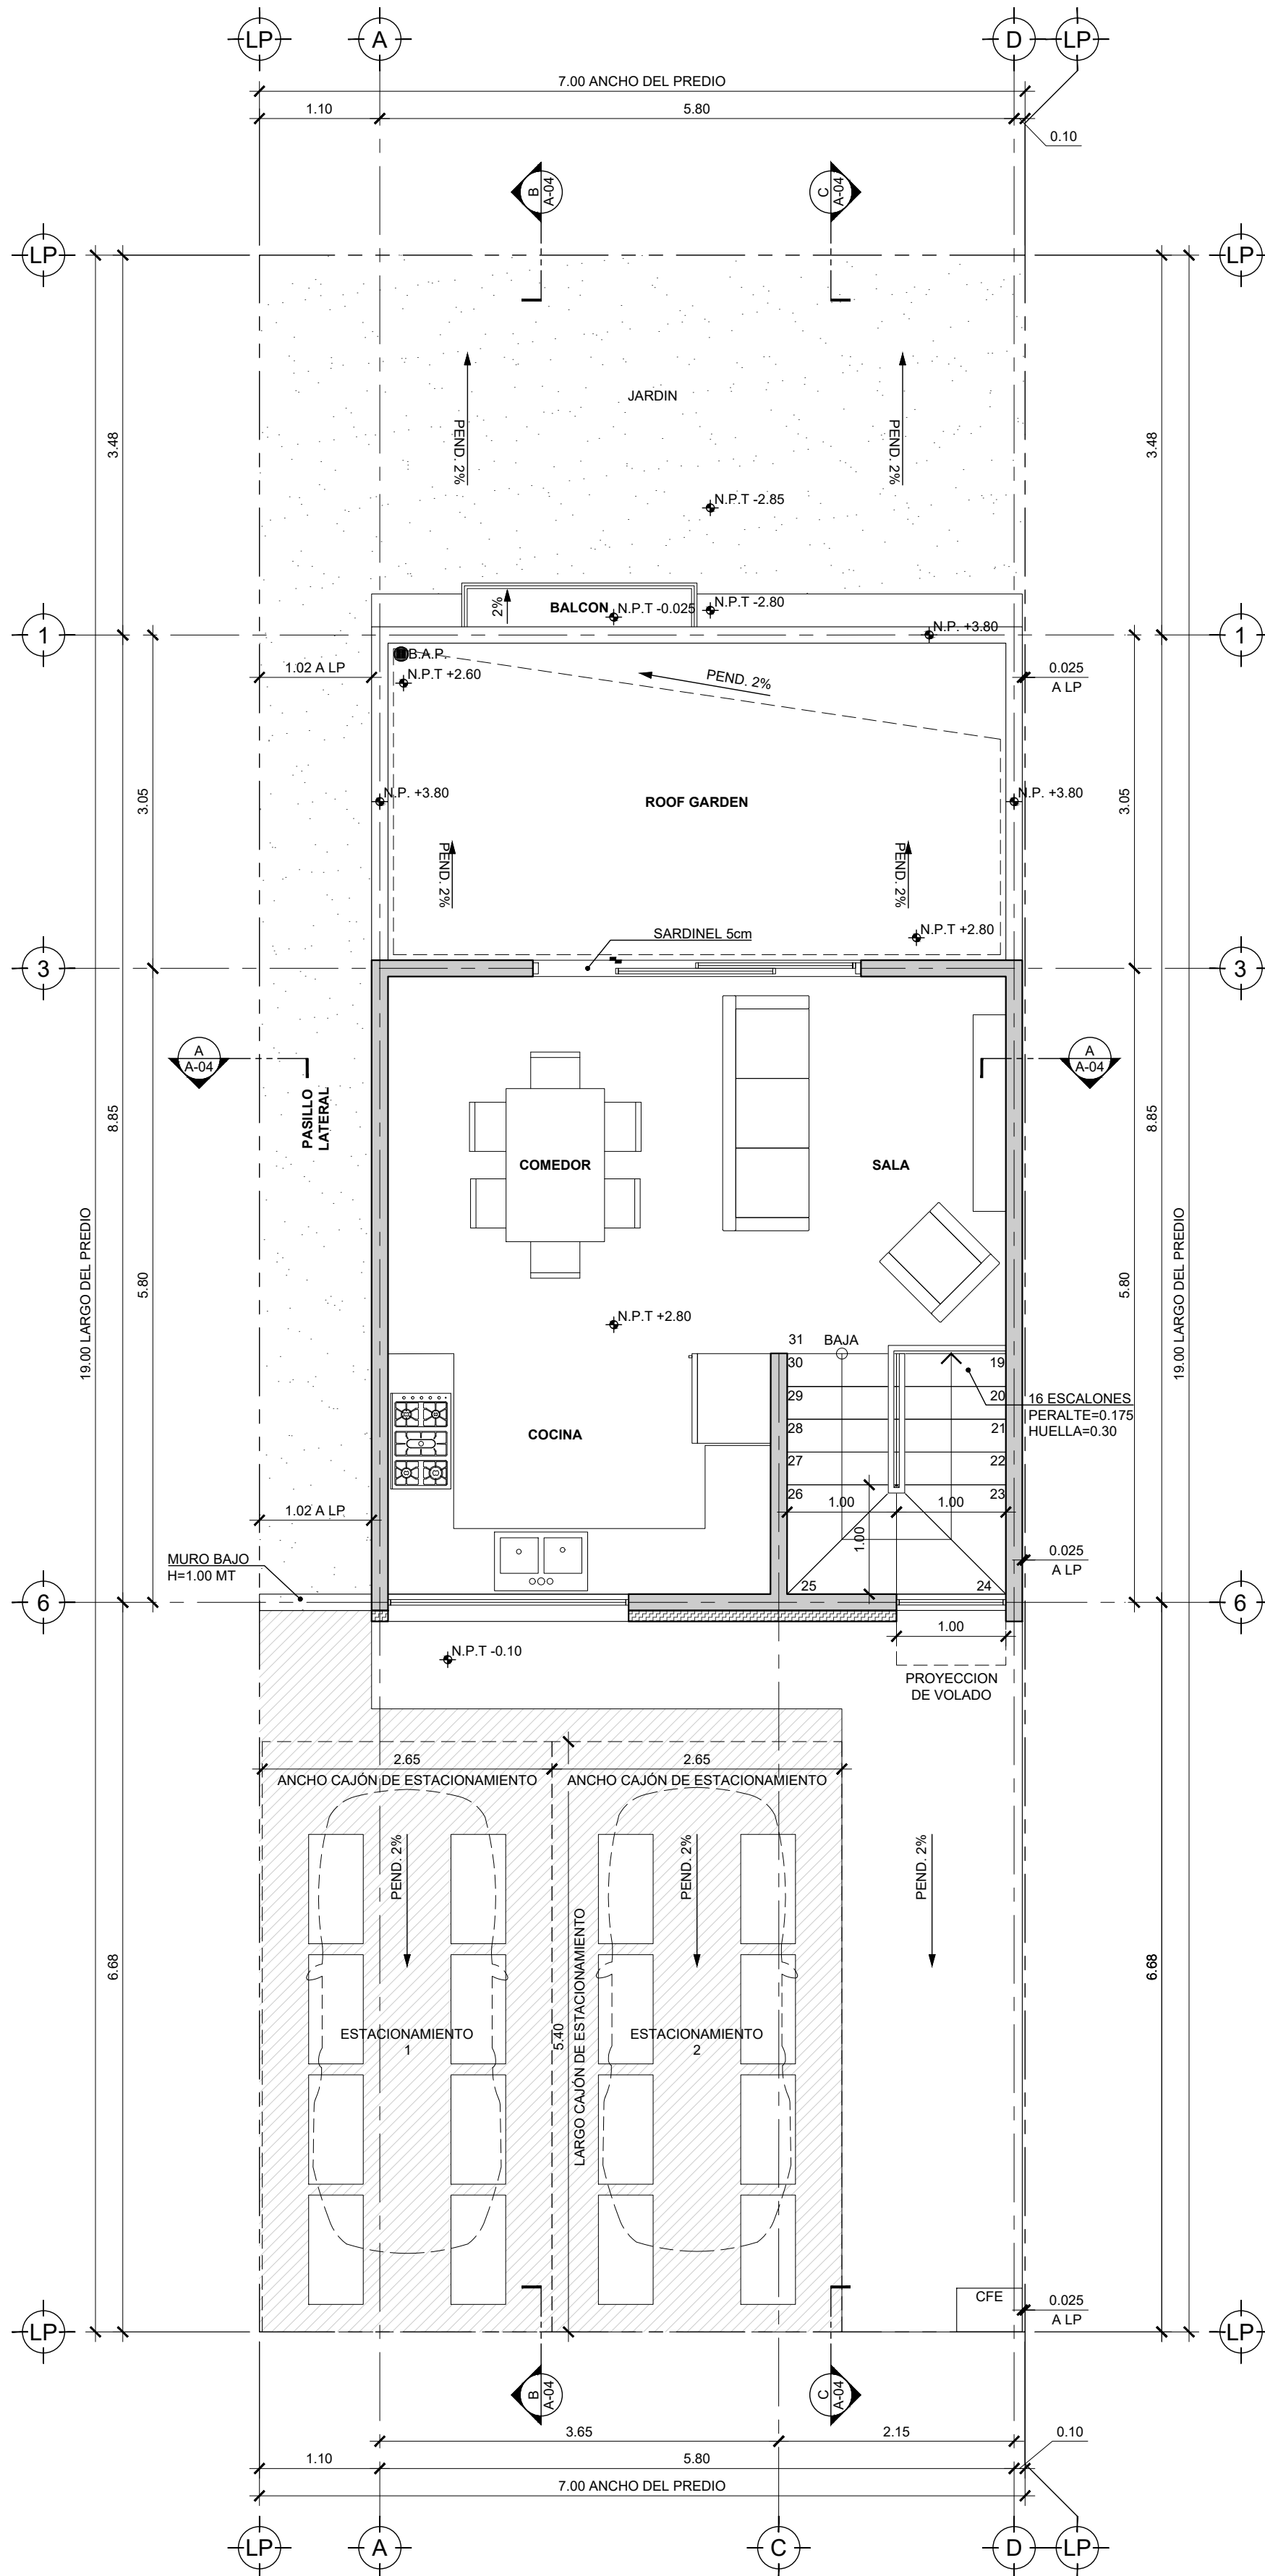

PLANTA ALTA
ESC 1:50

CUADRO DE ÁREAS	
ÁREA	ESPACIO
53.55m²	NIVEL -1
11.90m²	RECAMARA 1
12.25m²	RECAMARA 2
4.41m²	CUARTO DE LAVAR
6.98m²	ESTUDIO
3.67m²	BAÑO
7.30m²	ESCALERAS
7.04m²	MUROS NIVEL -1
48.41m²	PLANTA BAJA
12.67m²	RECAMARA PRINCIPAL
5.40m²	CLOSET
4.38m²	BAÑO PRINCIPAL
14.63m²	SALA
3.68m²	1/2 BAÑO
0.86m²	BALCÓN
6.79m²	MUROS PLANTA BAJA
35.40m²	PLANTA BAJA
19.48m²	SALA-COMEDOR
7.69m²	COCINA
4.40m²	ESCALERAS
3.83m²	MUROS PLANTA ALTA
137.36m²	TOTAL

DATOS

NORTE

ÁREA DE TERRENO 140.00 m2 (7.00 m x 19.00 m)

SUP. CONSTRUCCIÓN 137.36m²

- LIMITE DE PROPIEDAD
- ESCALERA (SUBE-BAJA)
- CAMBIO DE NIVEL
- + NIVEL EN PLANTA
- N.P.T. NIVEL DE PISO TERMINADO
- N.L.B.L. NIVEL DE LECHO BAJO DE LOSA
- NP NIVEL DE PRETIL
- LP LIMITE DE PROPIEDAD
- [M] UBICACIÓN DE MEDIDOR

Grupo Lagsa

Carretera Libre Tijuana Ensenada, K. M. 19.5, Col. Plan Libertad, Playas de Rosarito, B. C., México C. P. 22730 Tel: (661) 613.5005

Residencial San Marino

Carretera Escuintla Tijuana Ensenada, K. M. 23.5, Col. Playas de Tijuana, B. C., México, Tel: (664) 630-2777

PROYECTO PROTOTIPO CATANIA

SITUACIÓN TIJUANA, B.C.

PÉRITO ING. MARCO ANTONIO GONZÁLEZ PIÑUELAS

PLANO PLANTAS ARQUITECTÓNICAS

FECHA MAYO 2022

CLIENTE INSIGNIA PLACES S.A. DE C.V.

DIRECCIÓN FRACC. RESIDENCIAL SAN MARINO IV

NO. DE PÉRITO 405

ACOTACIÓN METROS

ESCALA 1:50