




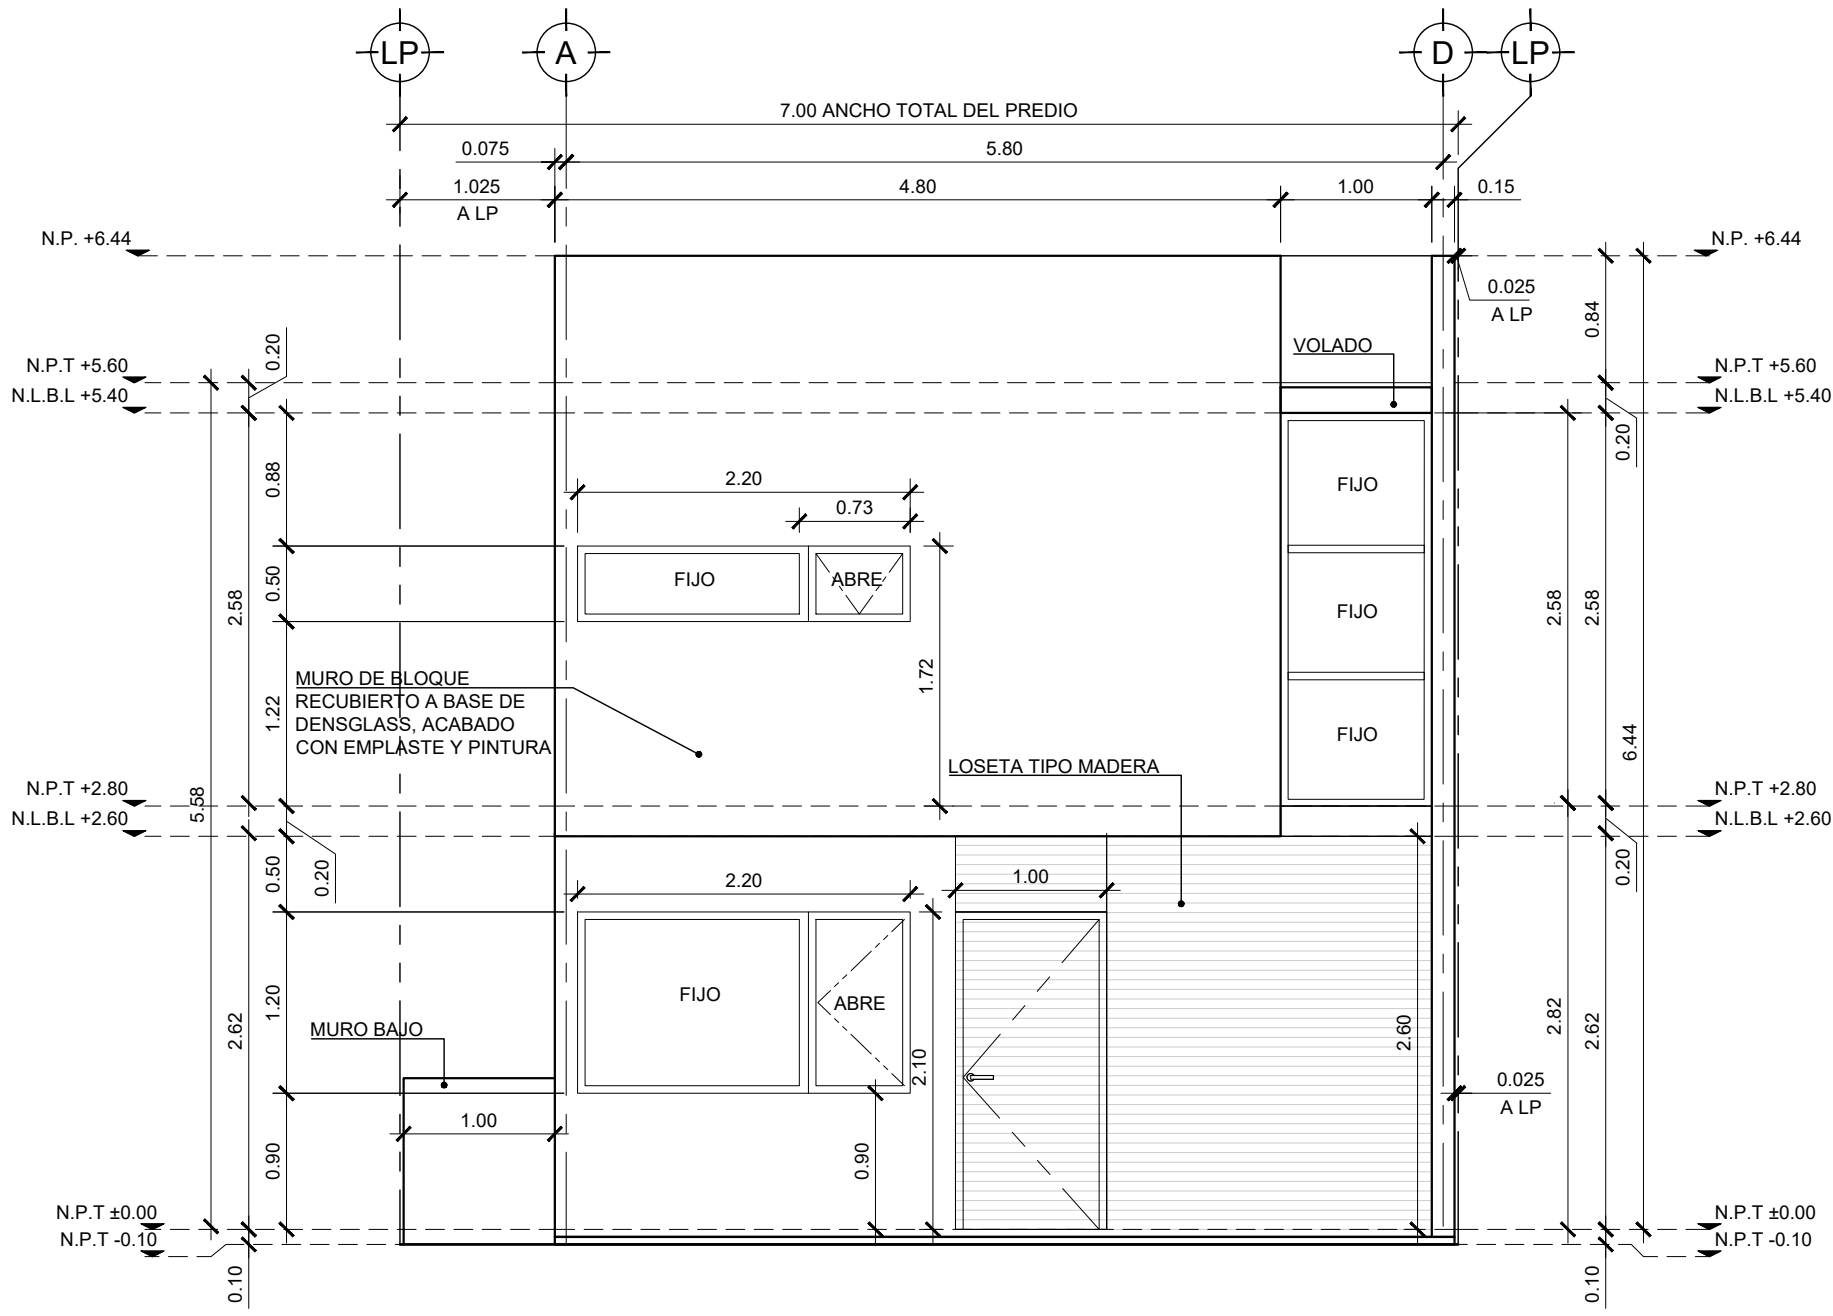

FACHADA FRONTAL
ESC 1:50

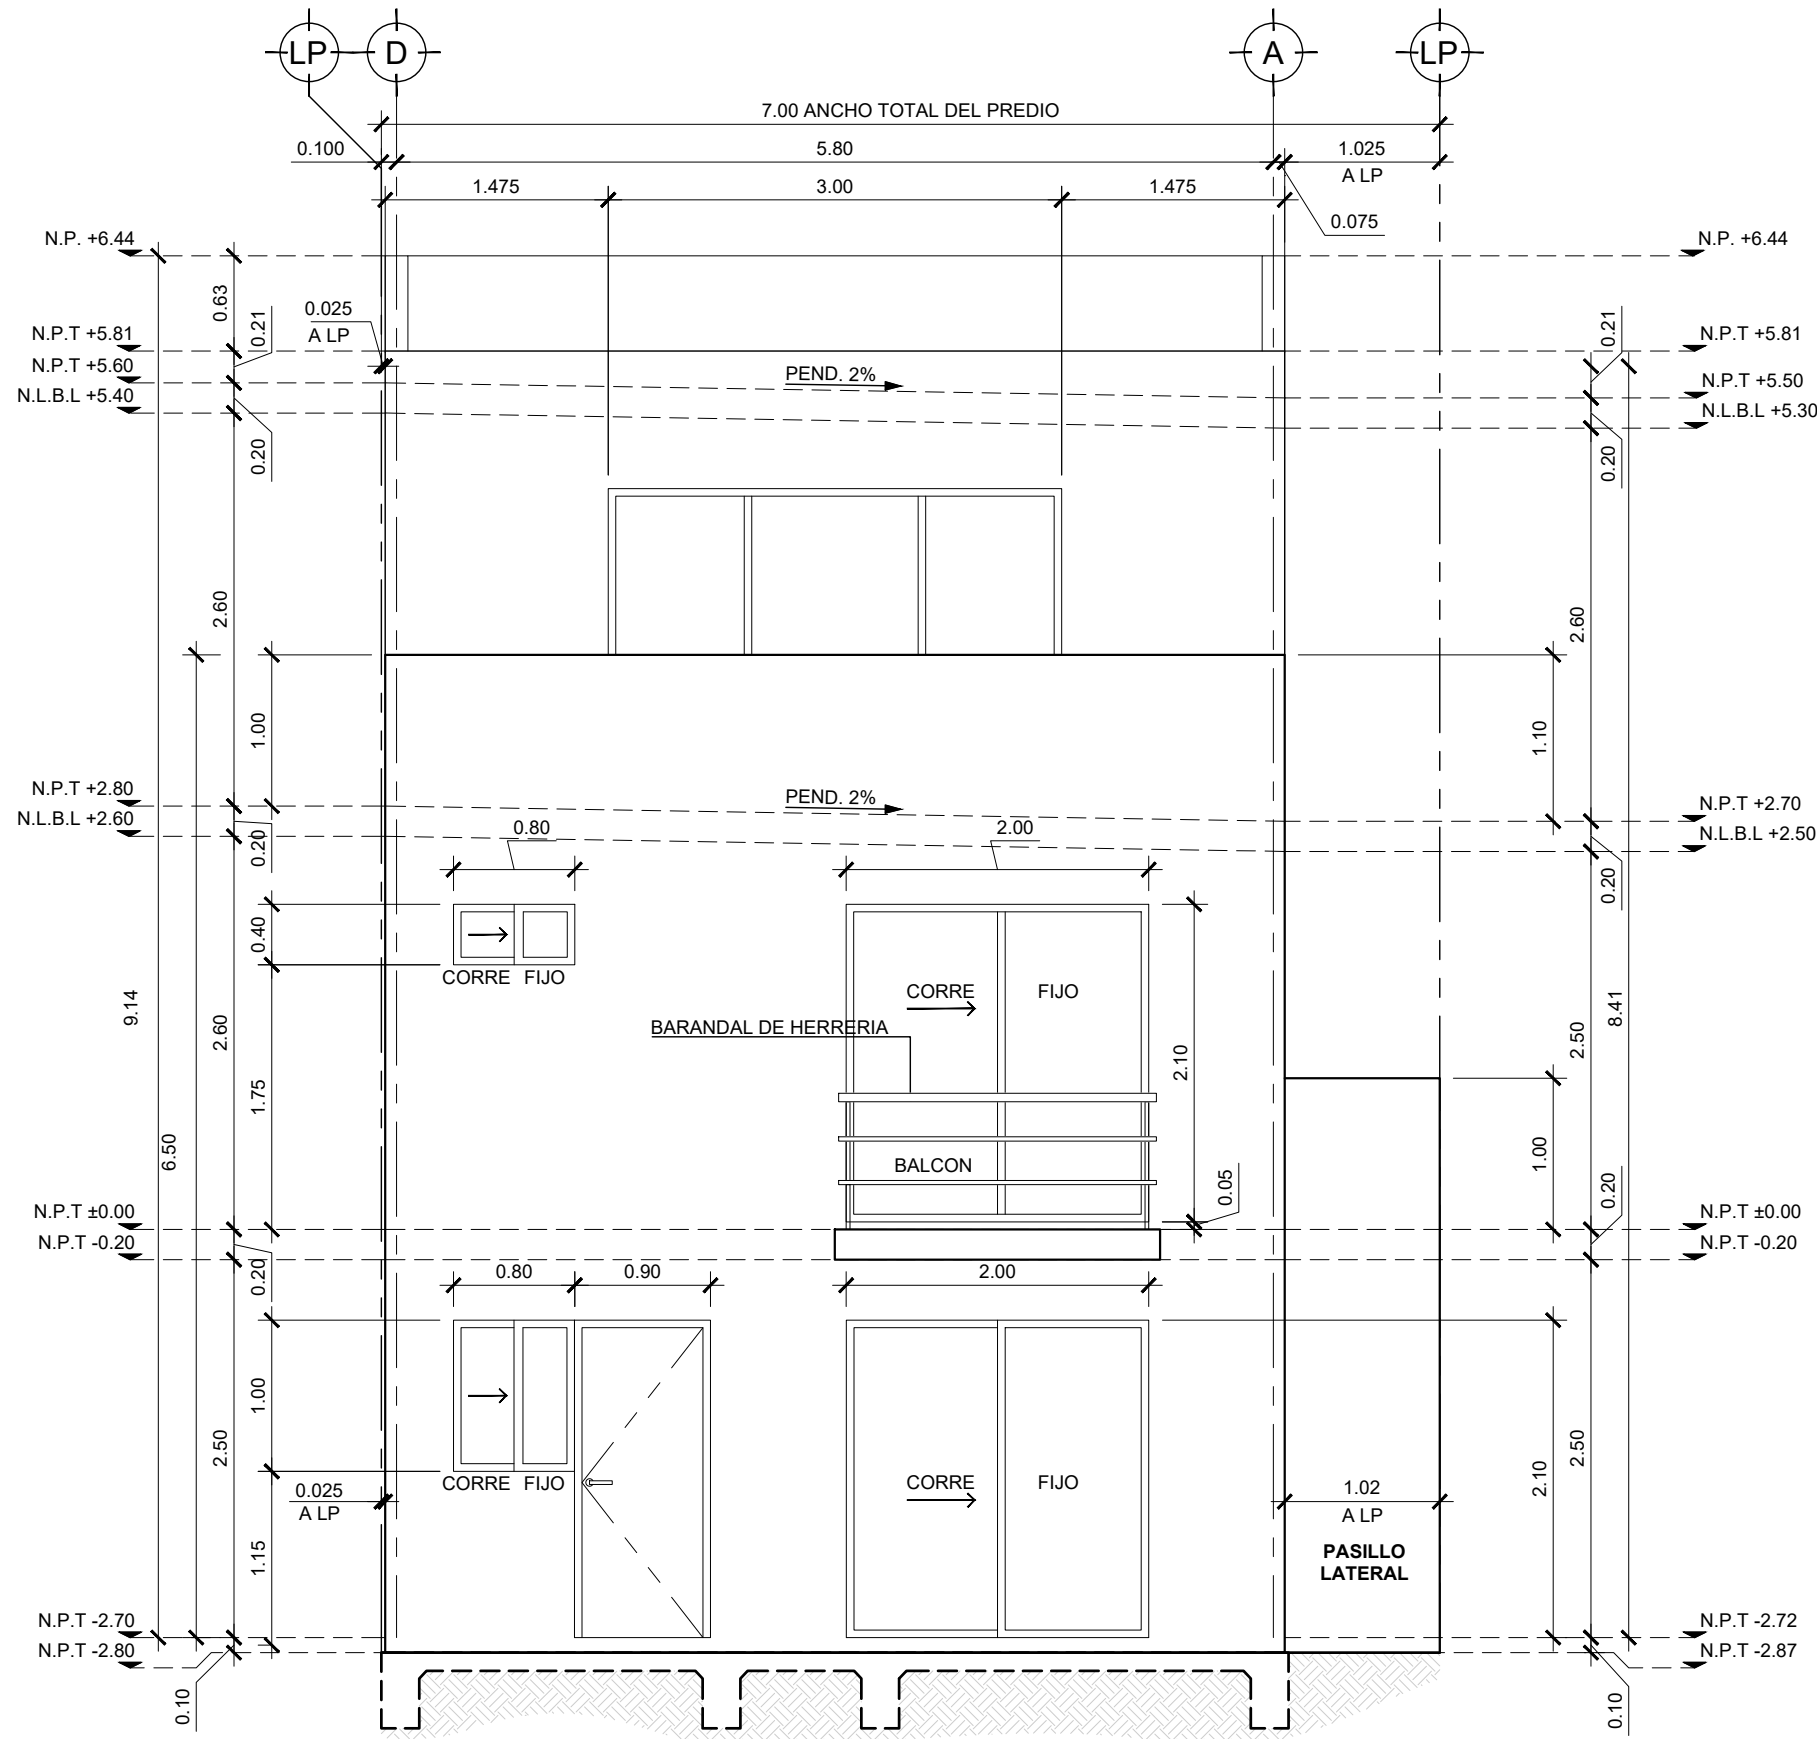

FACHADA TRASERA
ESC 1:50

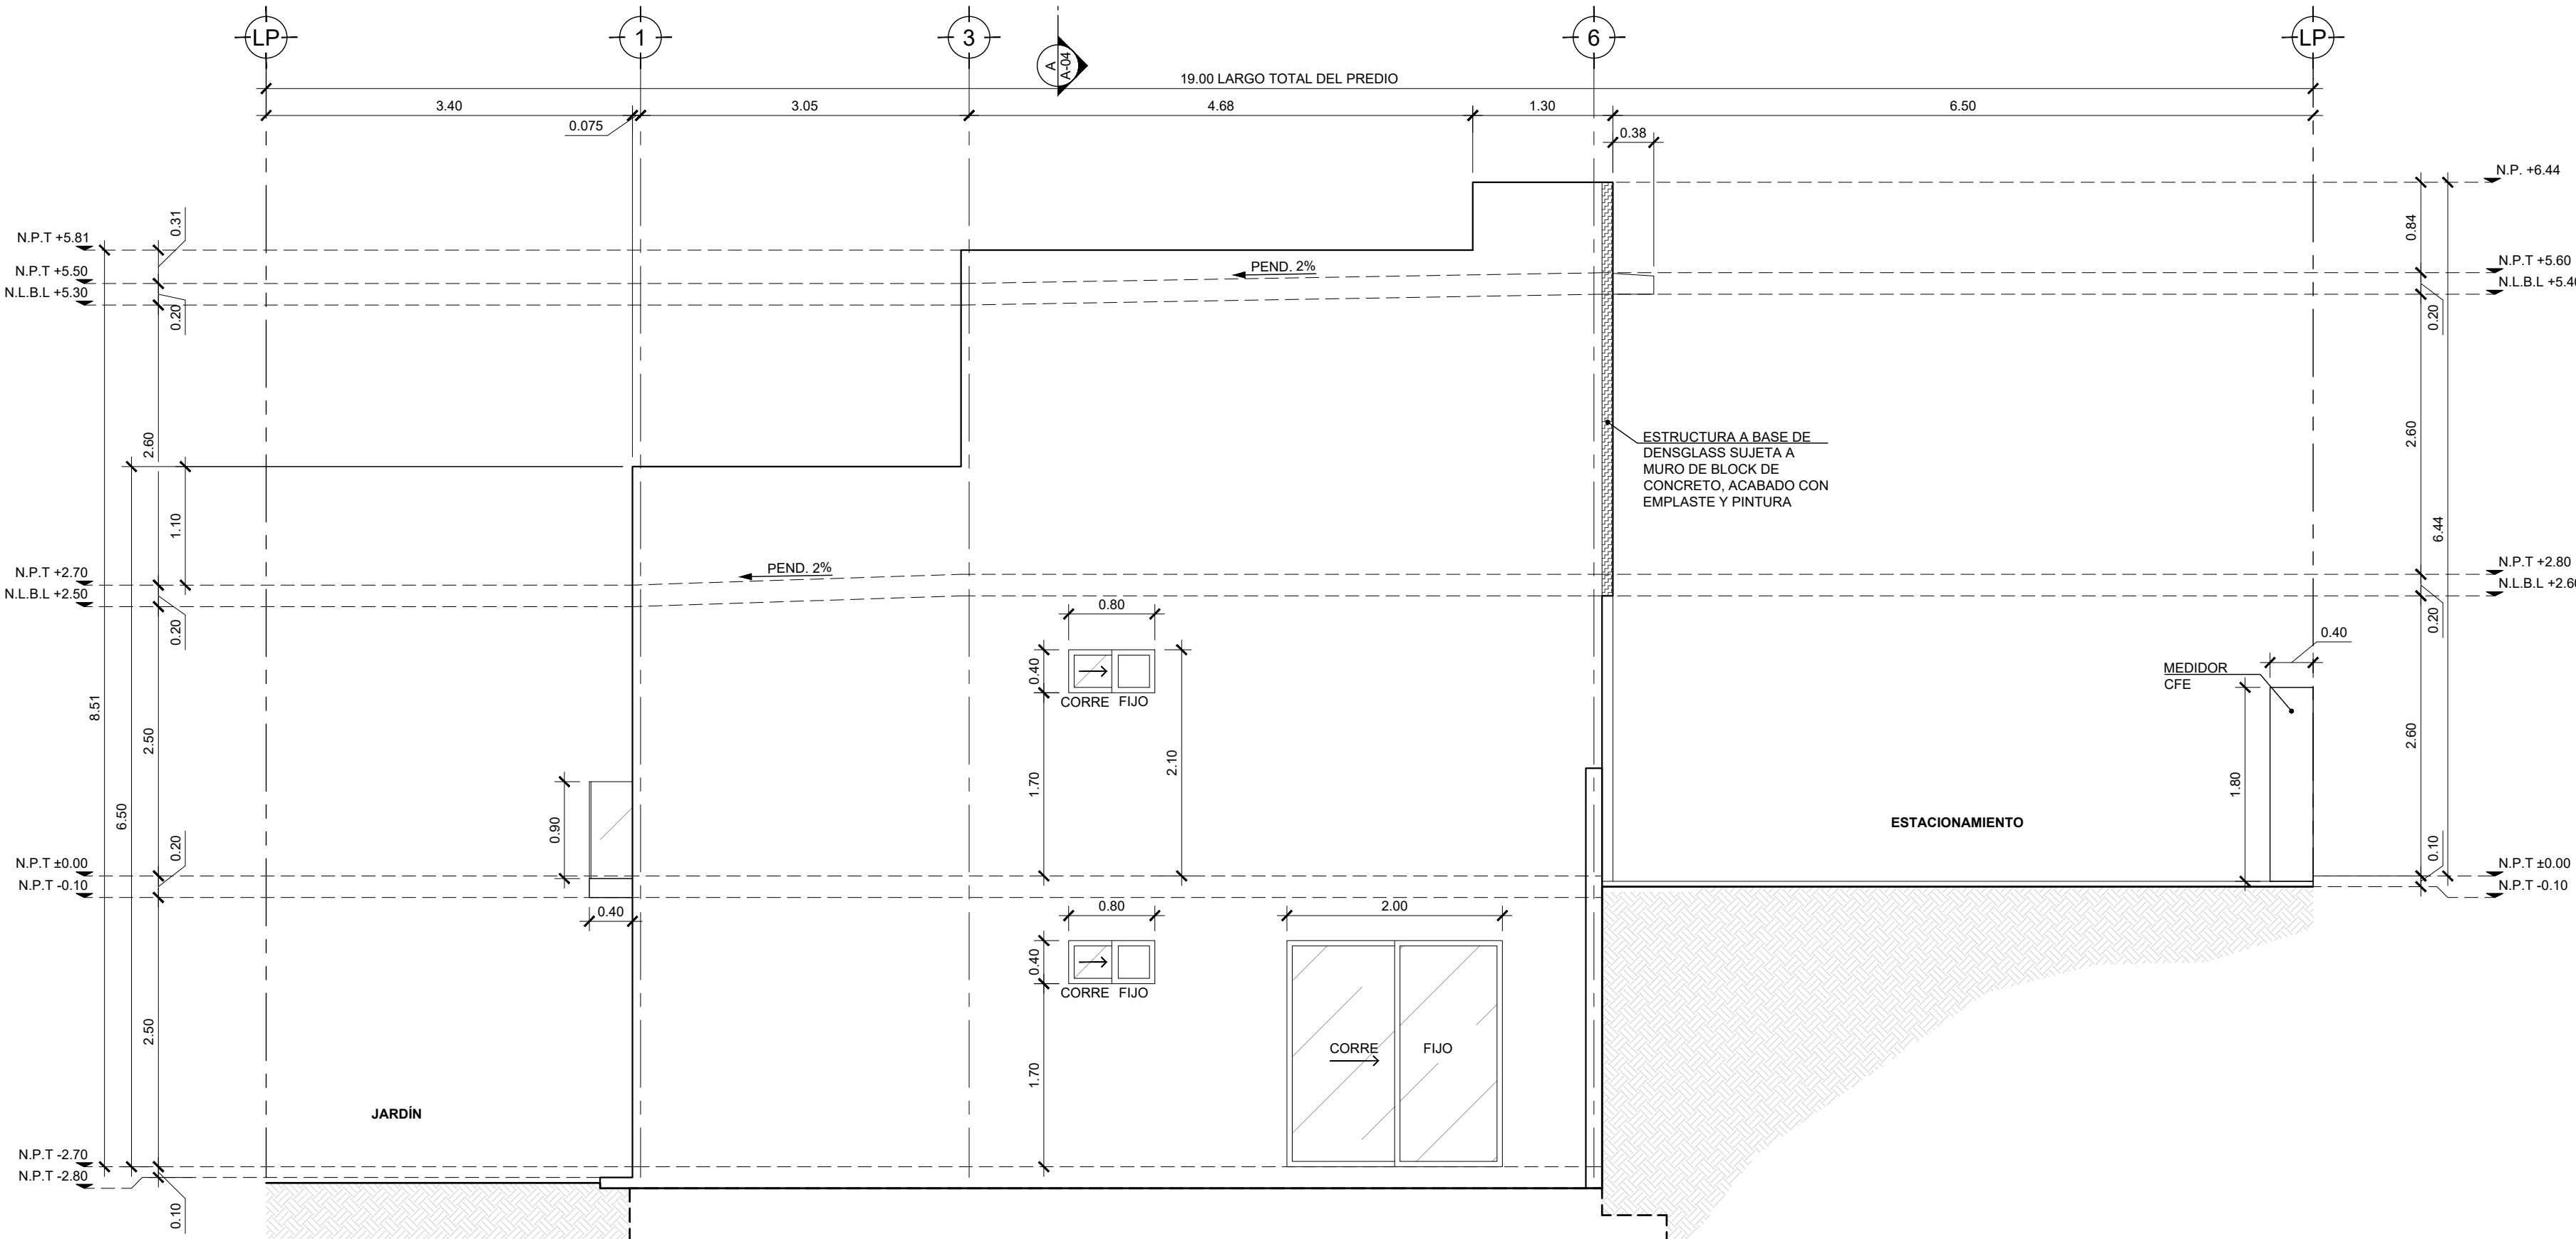

FACHADA LATERAL IZQUIERDA
ESC 1:50

DATOS



ÁREA DE TERRENO 140.00 m2 (7.00 m x 19.00 m)
SUP. CONSTRUCCIÓN 137.36m²

- LIMITE DE PROPIEDAD
- ESCALERA (SUBE-BAJA)
- CAMBIO DE NIVEL
- + NIVEL EN PLANTA
- N.P.T. NIVEL DE PISO TERMINADO
- N.L.B.L. NIVEL DE LECHO BAJO DE LOSA
- NP NIVEL DE PRETIL
- LP LIMITE DE PROPIEDAD
- UBICACIÓN DE MEDIDOR



Carretera Libre Tijuana Ensenada K. M. 19.5, Col. Plan Libertad Playas de Rosarito, B. C., México C. P. 22730 Tel: (661) 613.5005



Carretera Escuintla Tijuana Ensenada K. M. 23.5, Col. Playas de Tijuana, B. C., México Tel: (661) 613-2777

PROYECTO PROTOTIPO CATANIA
SITUACIÓN TIJUANA, B.C.

CLIENTE INSIGNIA PLACES S.A. DE C.V.
DIRECCIÓN FRACC. RESIDENCIAL SAN MARINO IV

PÉRITO ING. MARCO ANTONIO GONZÁLEZ PIÑUELAS

NO. DE PÉRITO 405

PLANO FACHADAS

FECHA MAYO 2022

ESCALA 1:50

ACOTACIÓN METROS

A-2