
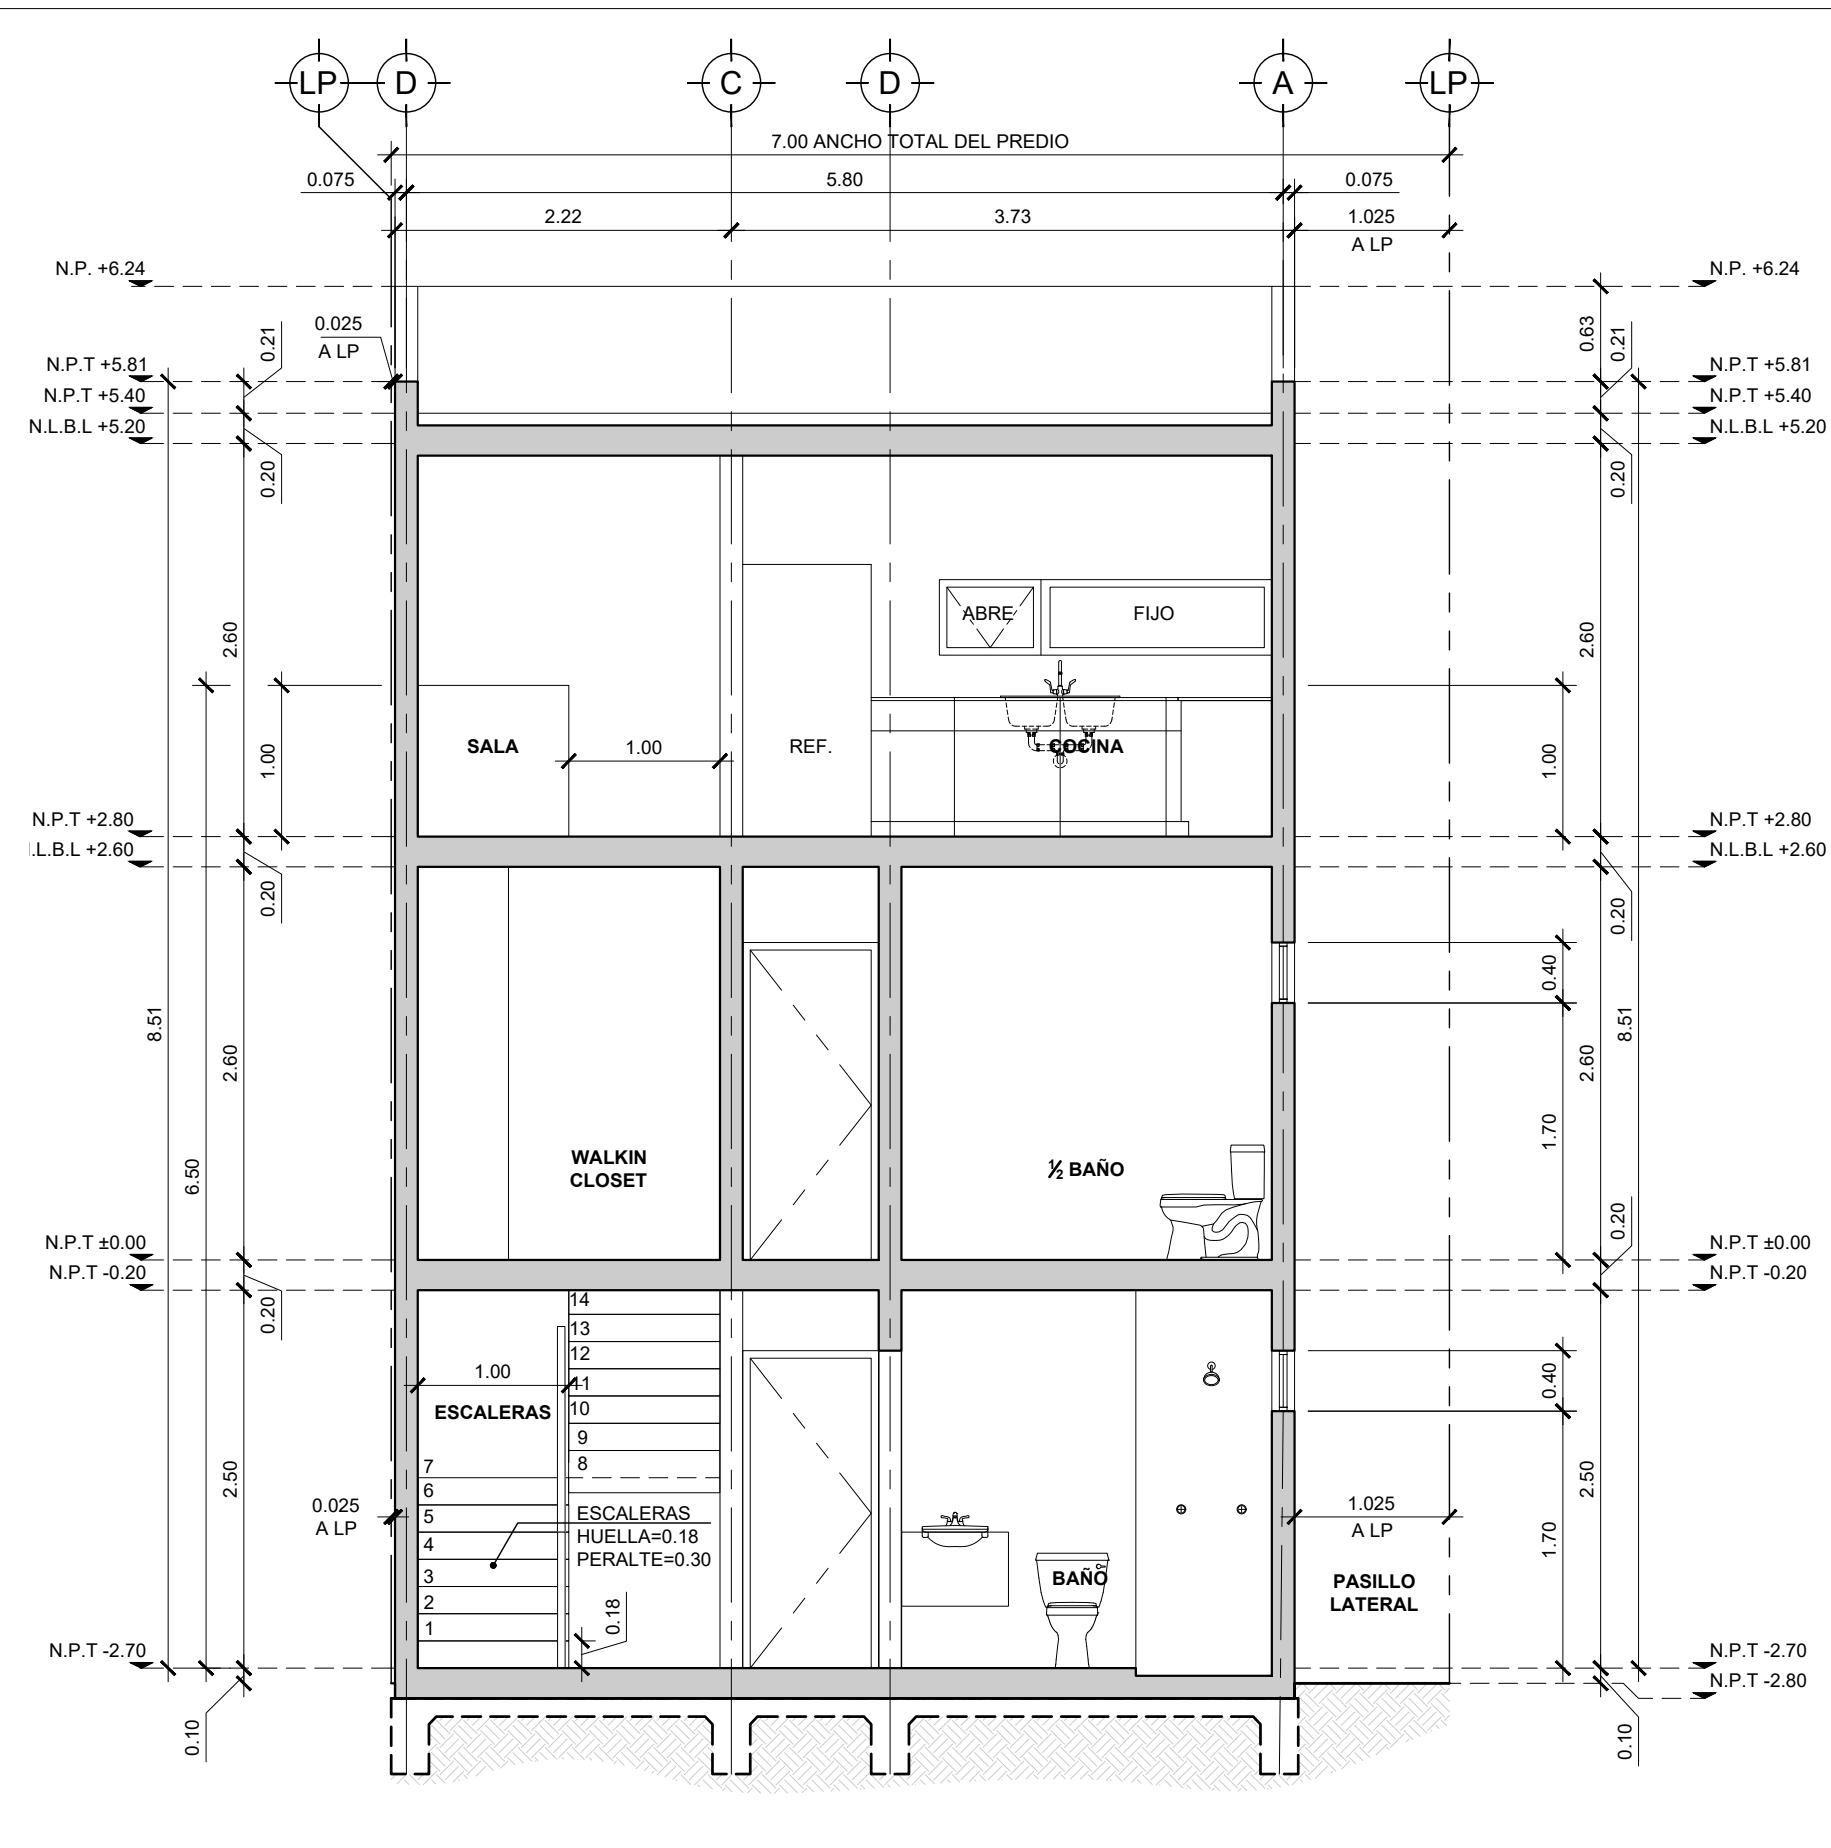
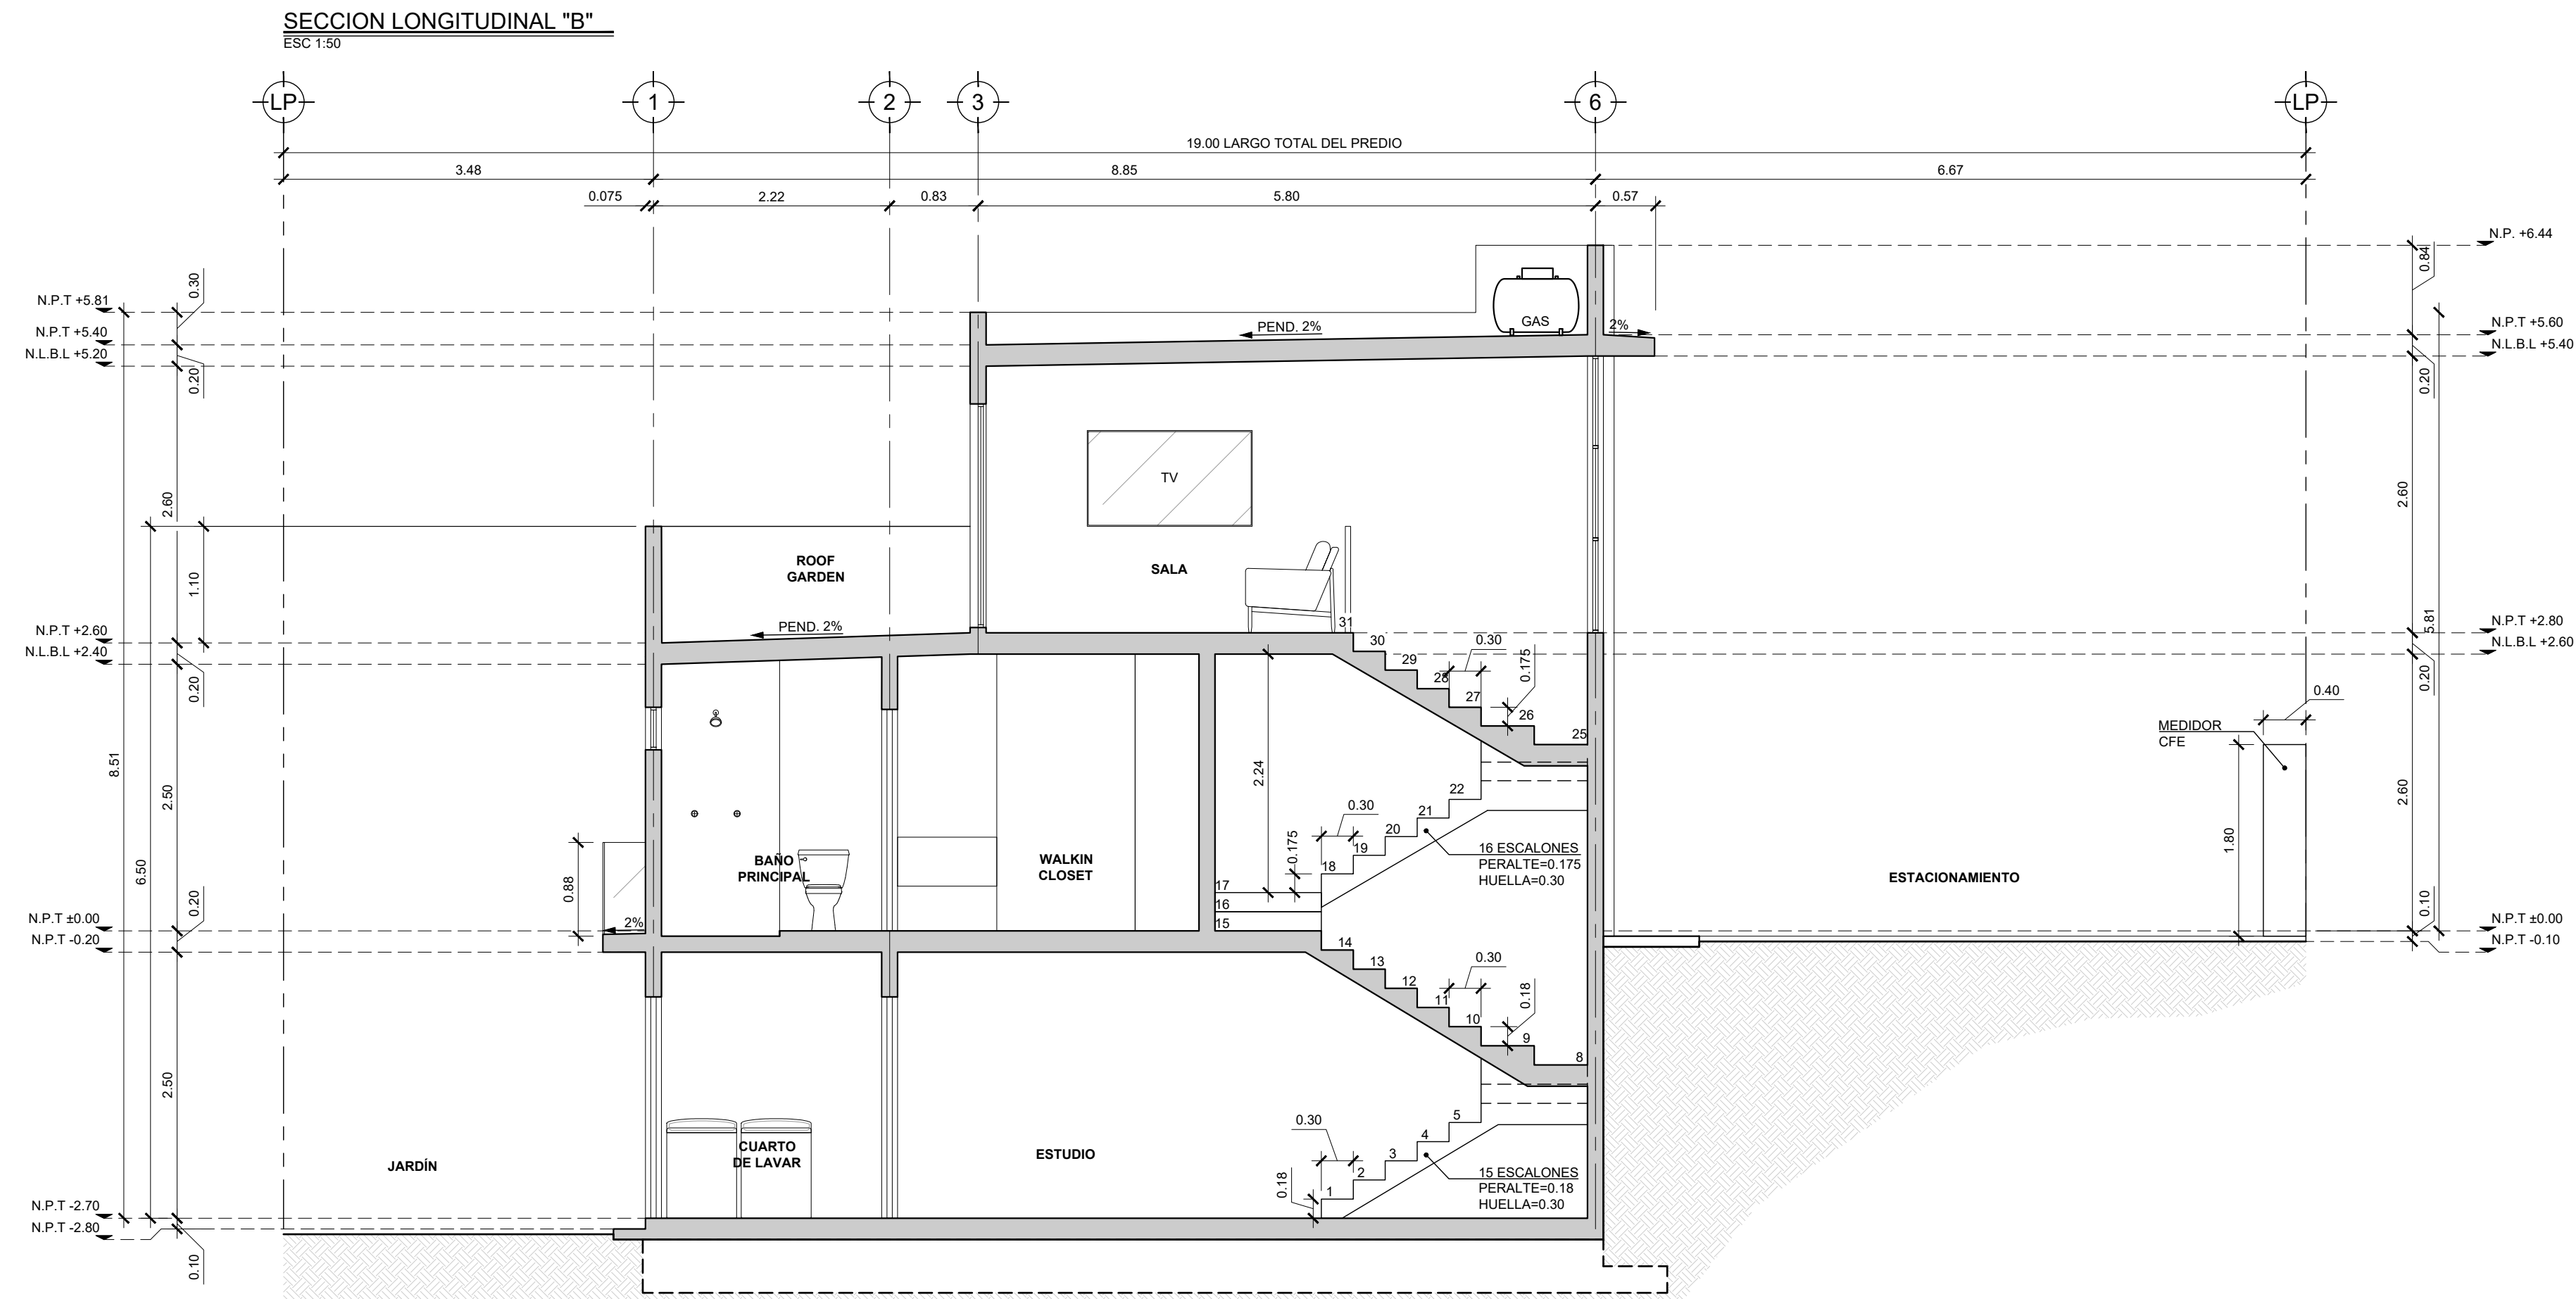


DATOS	
ÁREA DE TERRENO	140.00 m ² (7.00 m x 19.00 m)
SUP. CONSTRUCCIÓN	137.36m ²
---	LIMITE DE PROPIEDAD
→	ESCALERA (SUBE-BAJA)
—	CAMBIO DE NIVEL
+	NIVEL EN PLANTA
N.P.T.	NIVEL DE PISO TERMINADO
N.L.B.L.	NIVEL DE LECHO BAJO DE LOSA
NP	NIVEL DE PRETIL
LP	LIMITE DE PROPIEDAD
M	UBICACIÓN DE MEDIDOR

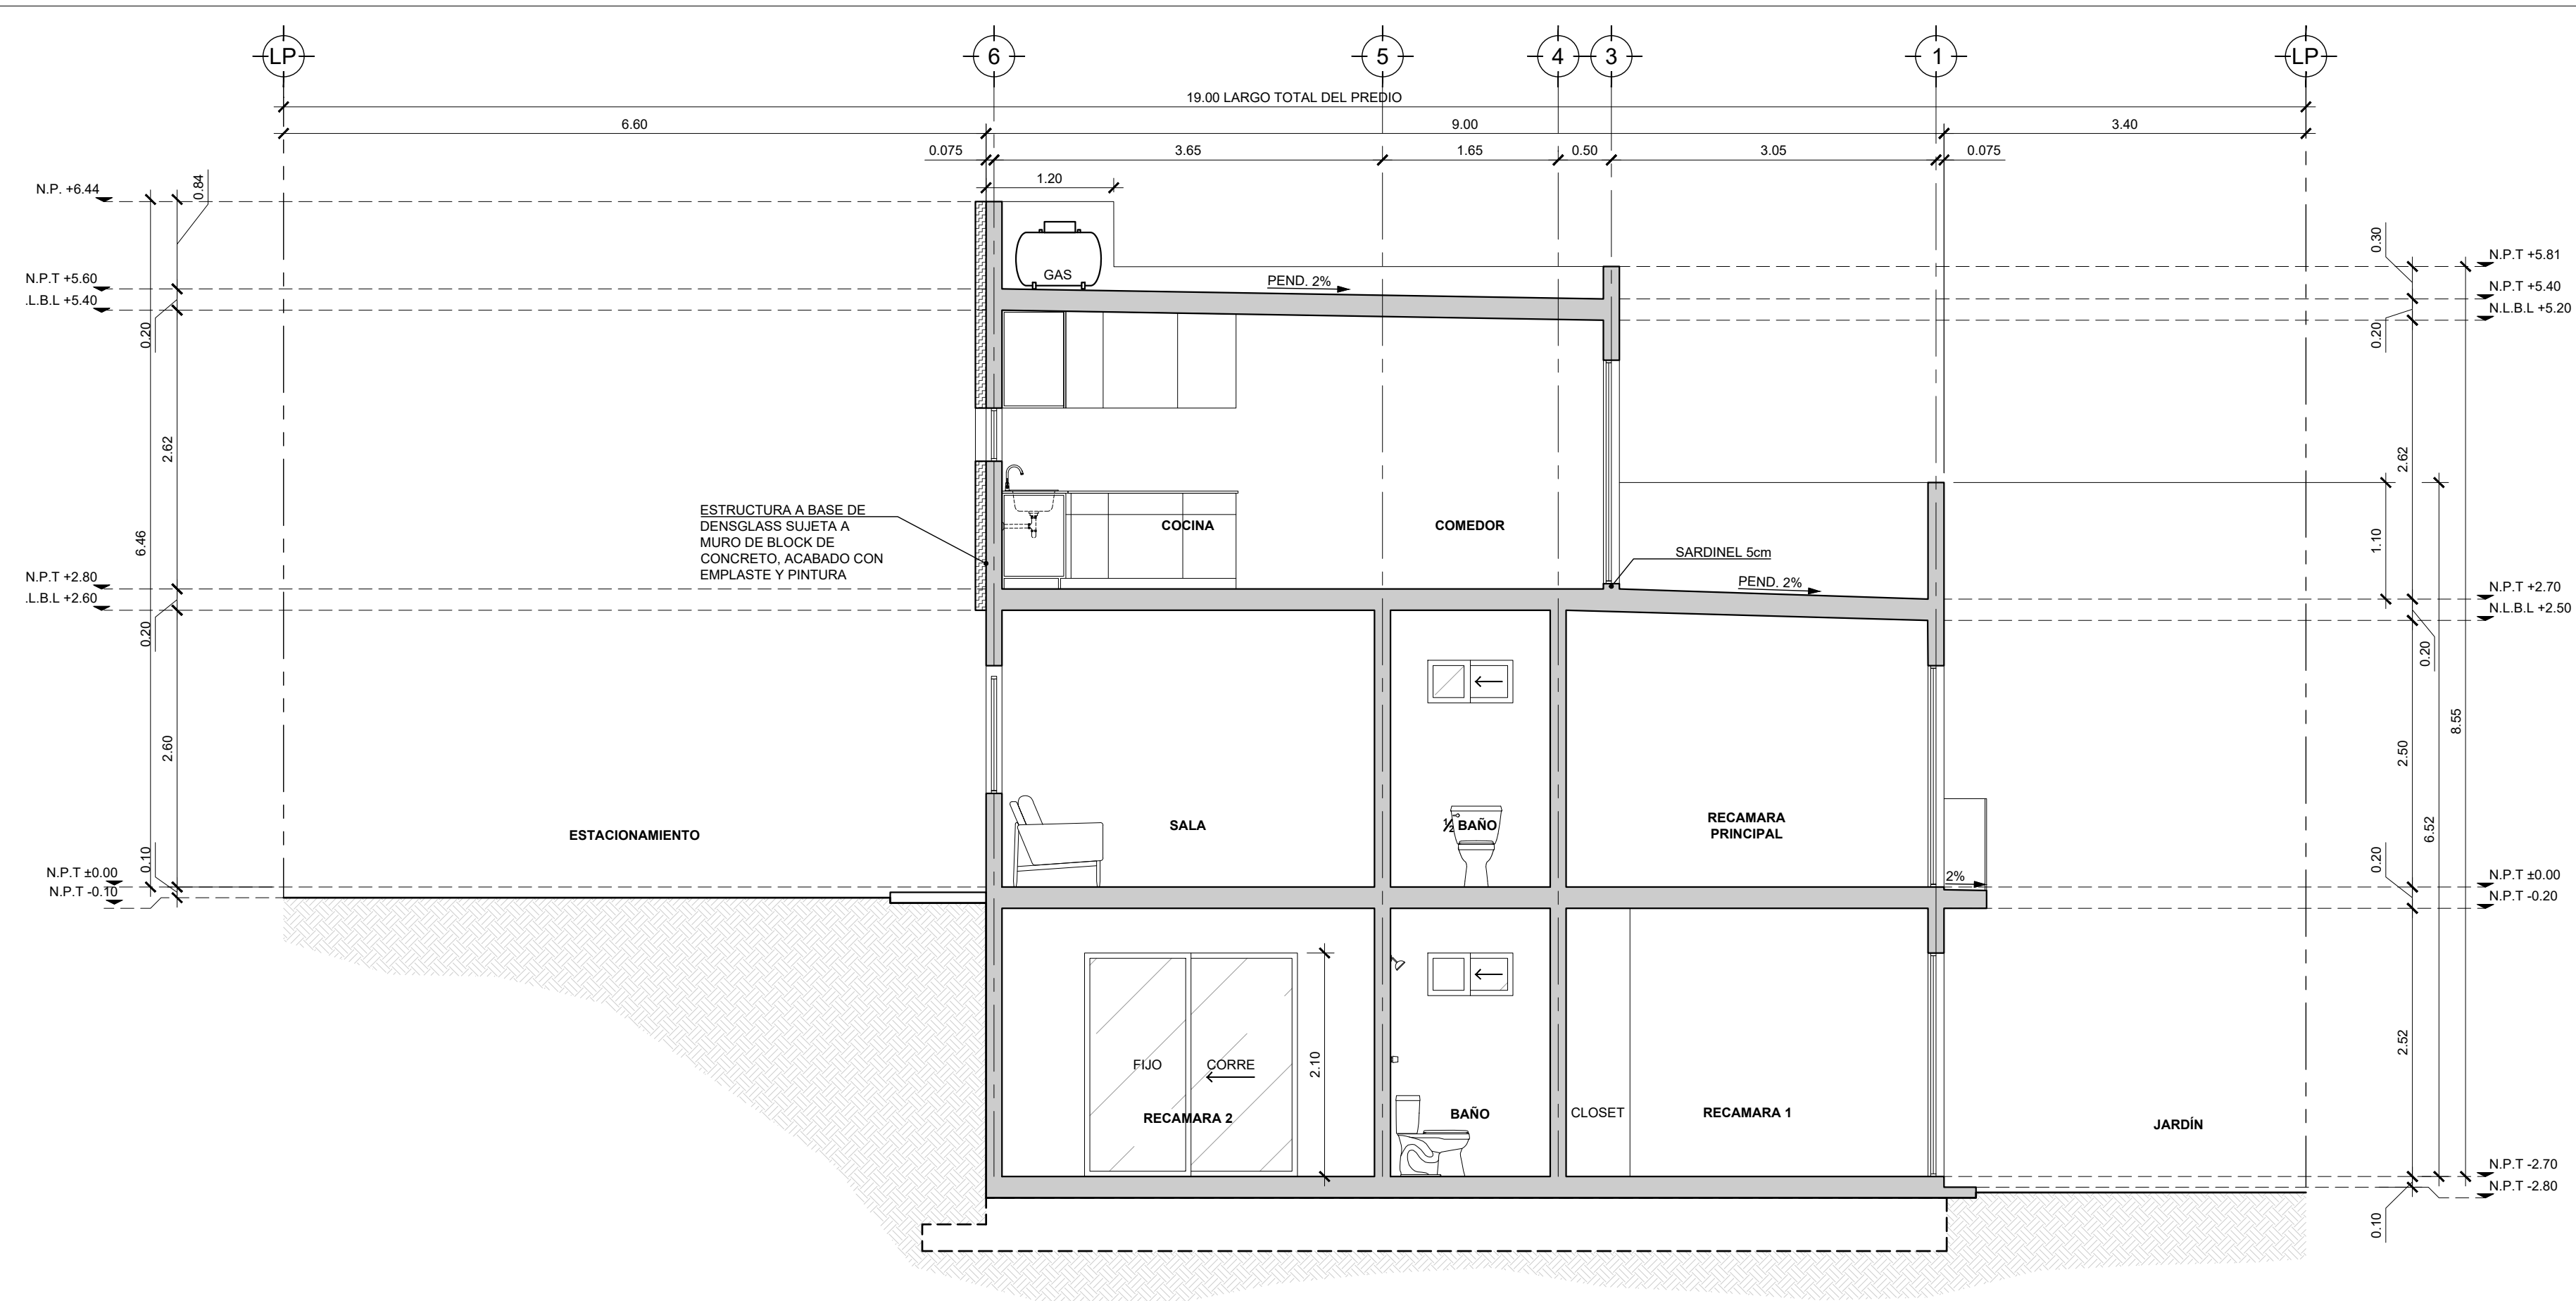

PROYECTO	PROTOTIPO CATANIA	CLIENTE	INSIGNIA PLACES S.A. DE C.V.
SITUACIÓN	TIJUANA, B.C.	DIRECCIÓN	FRACC. RESIDENCIAL SAN MARINO IV
PÉRITO	ING. MARCO ANTONIO GONZÁLEZ PIÑUELAS	NO. DE PÉRITO	405
PLANO	SECCIONES		
FECHA	MAYO 2022	ESCALA	1:50
		ACOTACIÓN	METROS